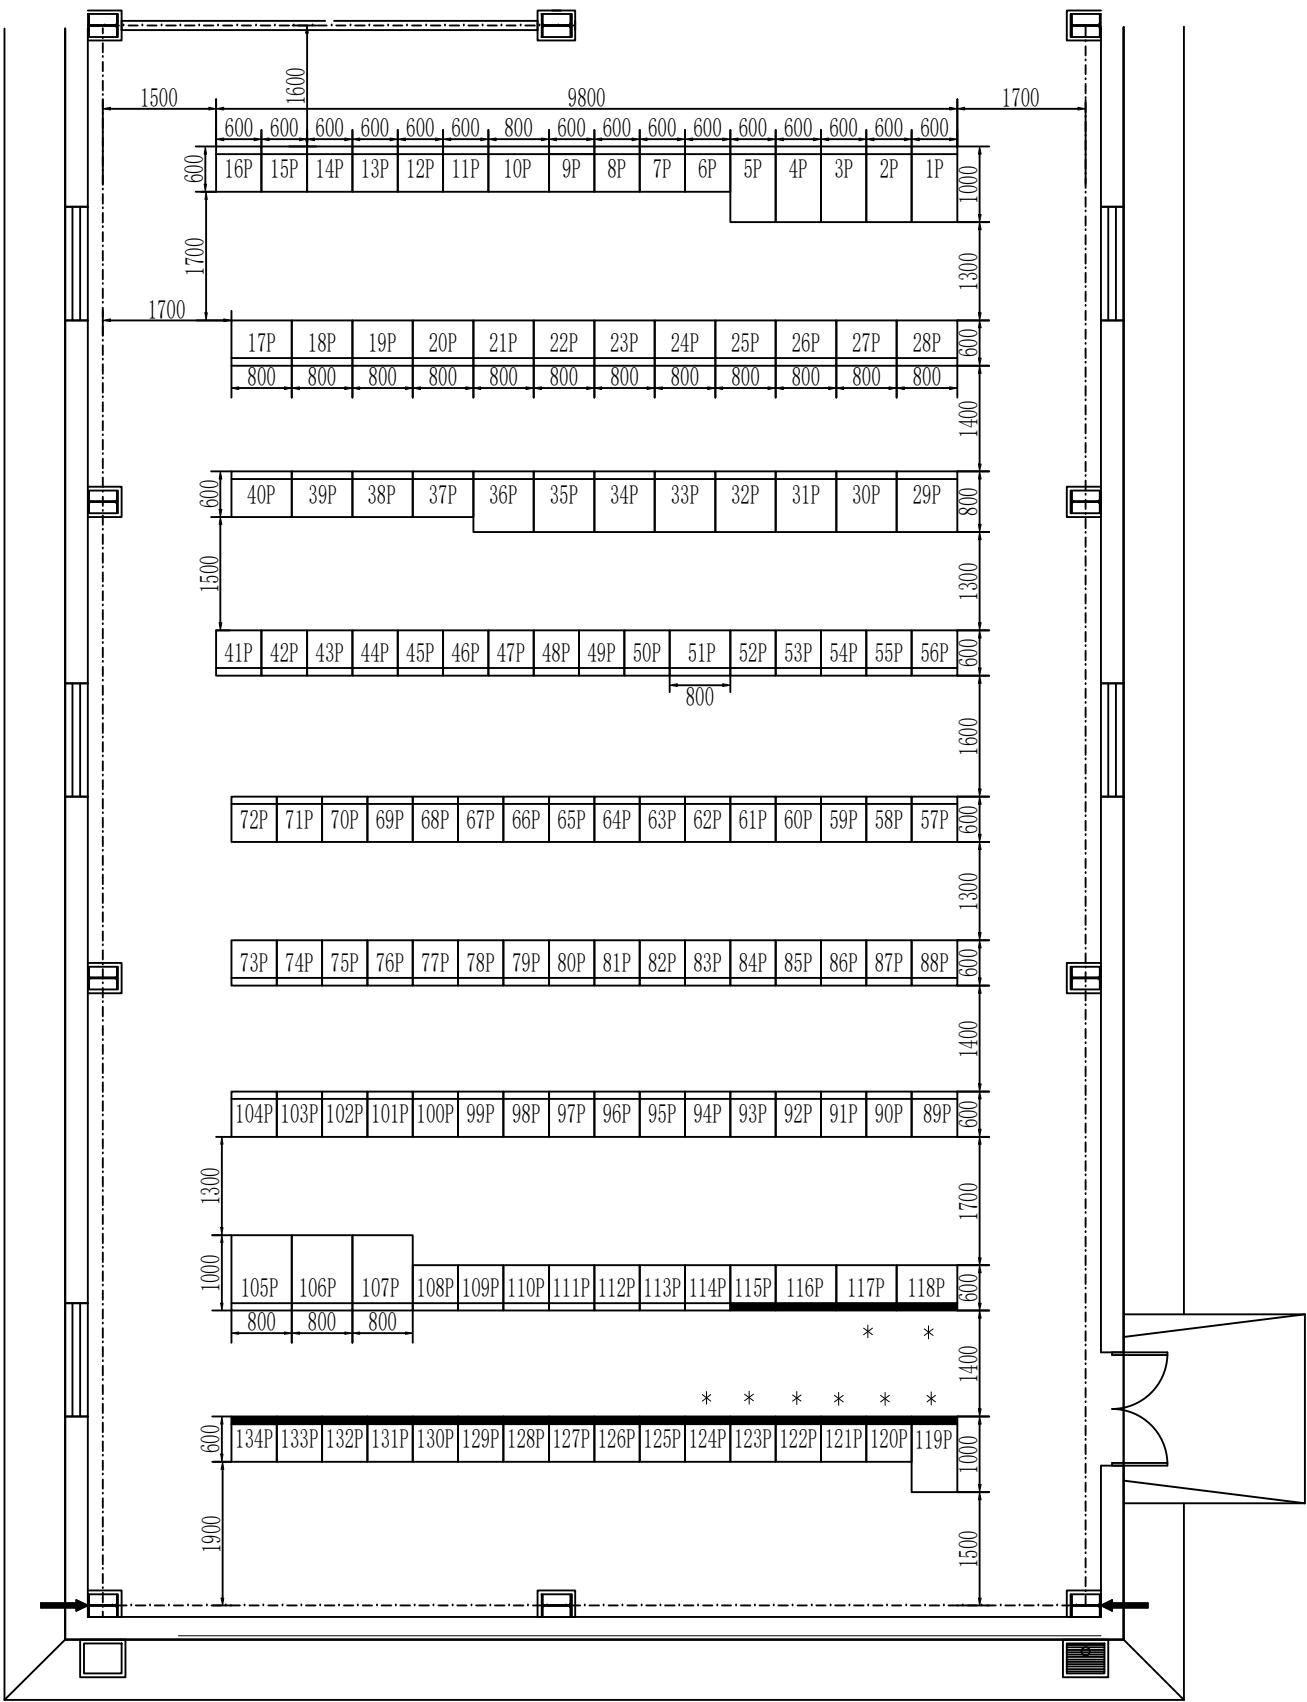


说明 1. 本站不设单独通信机房，通信设备安装在二次设备室内，光纤配线架屏柜尺寸建议采用2260mmx800mm（宽）x600mm，数据通信网屏柜尺寸建议采用2260mmx600mmx1000mm（深），其他屏柜尺寸建议采用2260mmx600mmx600mm。
2. 115P~134P 为通信屏柜，带*号部分为本期通信屏柜。
3. 二次屏柜布置以电气二次专业图纸为准。
4. 图纸标注单位为mm（毫米）。

通信屏柜用途一览表

屏号	名 称	型 式	数量	备 注
1~114P	电气二次屏位		114	二次屏，见电气二次设计
4P	调度数据网屏1		1	二次屏，见电气二次设计
5P	调度数据网屏2		1	二次屏，见电气二次设计
26P	UPS 电源系统屏1		1	二次屏，见电气二次设计
27P	UPS 电源系统屏2		1	二次屏，见电气二次设计
108P	220kV 光纤复用接口屏1		1	二次屏，见电气二次设计
109P	220kV 光纤复用接口屏2		1	二次屏，见电气二次设计
110P	110kV 光纤复用接口屏		1	二次屏，见电气二次设计
111P	通信电源屏1		1	由电气二次开列
112P	通信馈线屏1		1	由电气二次开列
113P	通信馈线屏2		1	由电气二次开列
114P	通信电源屏2		1	由电气二次开列
115P	通信备用屏		1	600宽，远期预留
116P	通信备用屏		1	800宽，远期预留
* 117P	ODF 配线架—1	ODF (480芯)	1	800宽
* 118P	ODF 配线架—2	ODF (480芯)	1	800宽
* 119P	数据通信网设备列 AD 设备屏		1	交流，1000深
* 120P	省网A1平面SDH 设备屏	华为E9624X	1	
* 121P	省网A2平面SDH 设备屏	中兴S385	1	
* 122P	数字配线架—1	DDF (160系统)	1	省网
* 123P	省网光电一体设备屏	MDP—3000D	1	
* 124P	音配线架	VDF (200回)	1	
* 125P	地网SDH 设备屏	阿尔卡特1660 CSS—16	1	
* 126P	数字配线架—2	DDF (64系统)		地网
* 127P	地网光电一体设备屏	MDP—3000D	1	
128P~134P	通信备用屏		10	远期预留

湖南经研电力设计有限公司			/工程		施工图设计阶段	
专业	会 签 人	日 期	批准	设计/勘测	二次设备室平面布置图（桃江西变）	
			审核	比例		
			校核	日期	图号	BA22015S-U0101-14

服务承诺：接到您通知1小时内予以答复并及时提供工代服务。服务电话：0731-85948331，0731-85948342。