



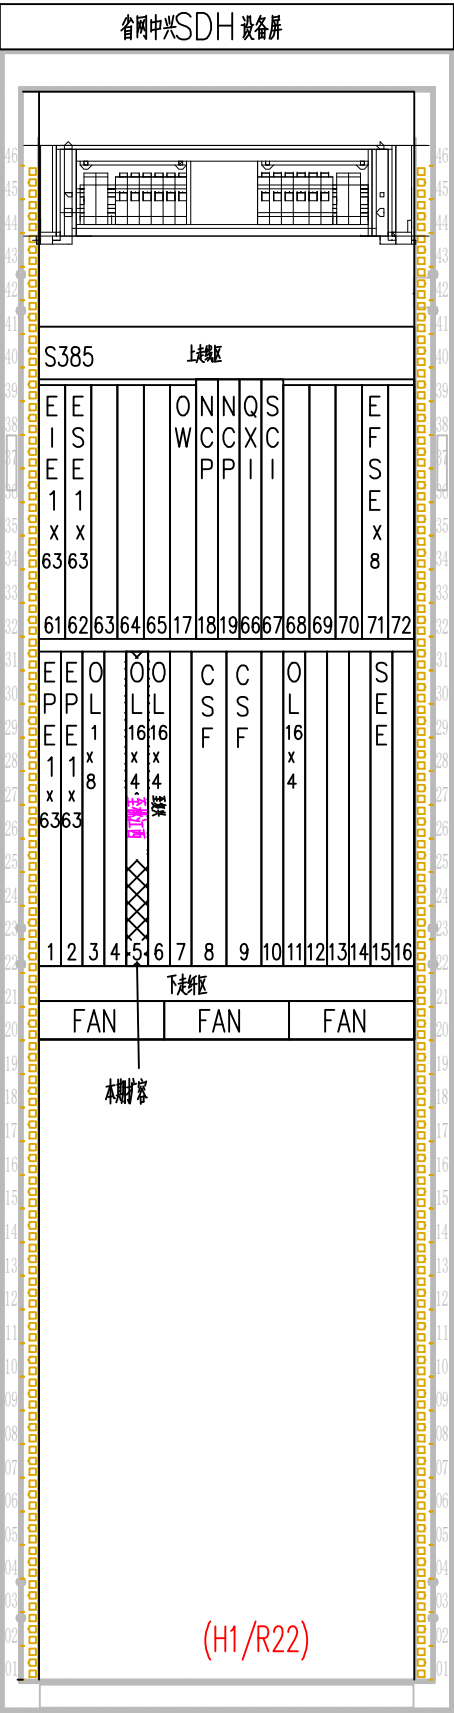

省网A2平面SDH设备机架图

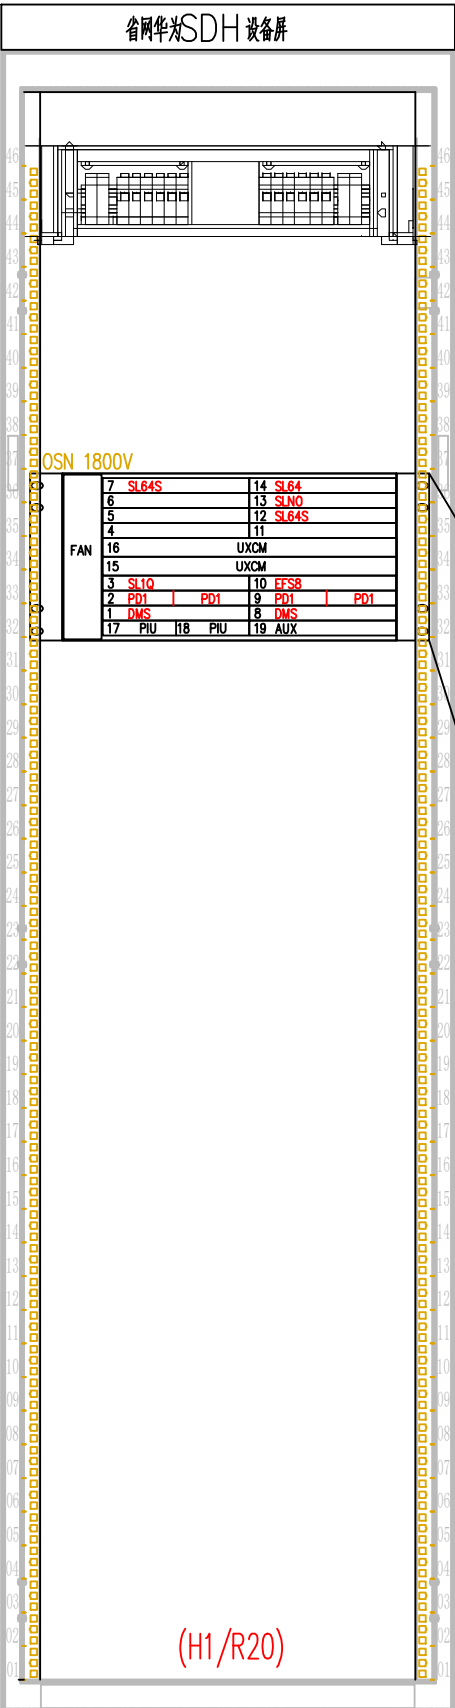

省网A1平面SDH设备机架图

主要业务板件型号一览表:

子架	型 号	描 述
OSN 1800V	PIU	电源板
	UXCM	主控交叉时钟合一板
	FAN	散热风扇
	AUX	辅助接口板
	DMS	32路E1/T1 电接口板
	PD1	32路E1/T1 支路业务处理板 (保护板)
	EFS8	8路E 以太网交换处理板
	SL1Q	4路STM-1 线路处理板
	SLNO	STM-16/STM-4/STM-1 业务处理板
	SL410	8路STM-4/STM-1 业务处理板
OSN 1800V	SL16Q	4路STM-16 线路处理板
	SL64S	1路STM-64 线路处理板

局部放大:

FAN	7	SL64S (复用)	14	SL64S (清江)
	6	SL16Q (横江西)	13	SLNO (刘家湾)
	5		12	SL64S (避丰桥)
	4		11	
	16	UXCM		
	15	UXCM		
	3	SL1Q (凌津滩)	10	EFS8
	2	PD1	9	PD1
	1	DMS	8	DMS
	17	PIU	18	PIU

主要业务板件型号一览表:

子架	型 号	描 述
S385	FAN	散热风扇
	OW	公务板
	NCP	网元控制板
	QXI	管理接口板
	SCI	时钟接口板
	CSF	F 型交叉与时钟处理板 (240G)
	ESE1x63	63路2M 接口板
	EIE1x63	63路2M 接口倒换板
	EPE1x63	63路2M 处理板
	ESFE x8	8路以太网电接口板
	SEC	以太网处理板
	OL64	1xSTM-64 光线路板
	OL16	1xSTM-16 光线路板
	OL4x4	4xSTM-4 光线路板

- 注: 1. 桃花江变现有省网A1平面SDH设备OSN 1800V (R20) 扩容4xSTM-16光接口板1块(含L16.2光模块1块), 对桃江西变。
2. 桃花江变现有省网A2平面SDH设备S385 (R22) 扩容4xSTM-16光接口板1块(含L16.2光模块1块), 对桃江西变。
3. 本图依据设备厂家提供资料编制, 请根据现场到货情况调整至本图布置方式。

 湖南经研电力设计有限公司				/工程		施工图设计阶段
批准		设计/勘测		省网SDH设备机架布置图(桃花江变)		
审核		比例				
校核		日期		图号	BA22015S-U0101-32	