


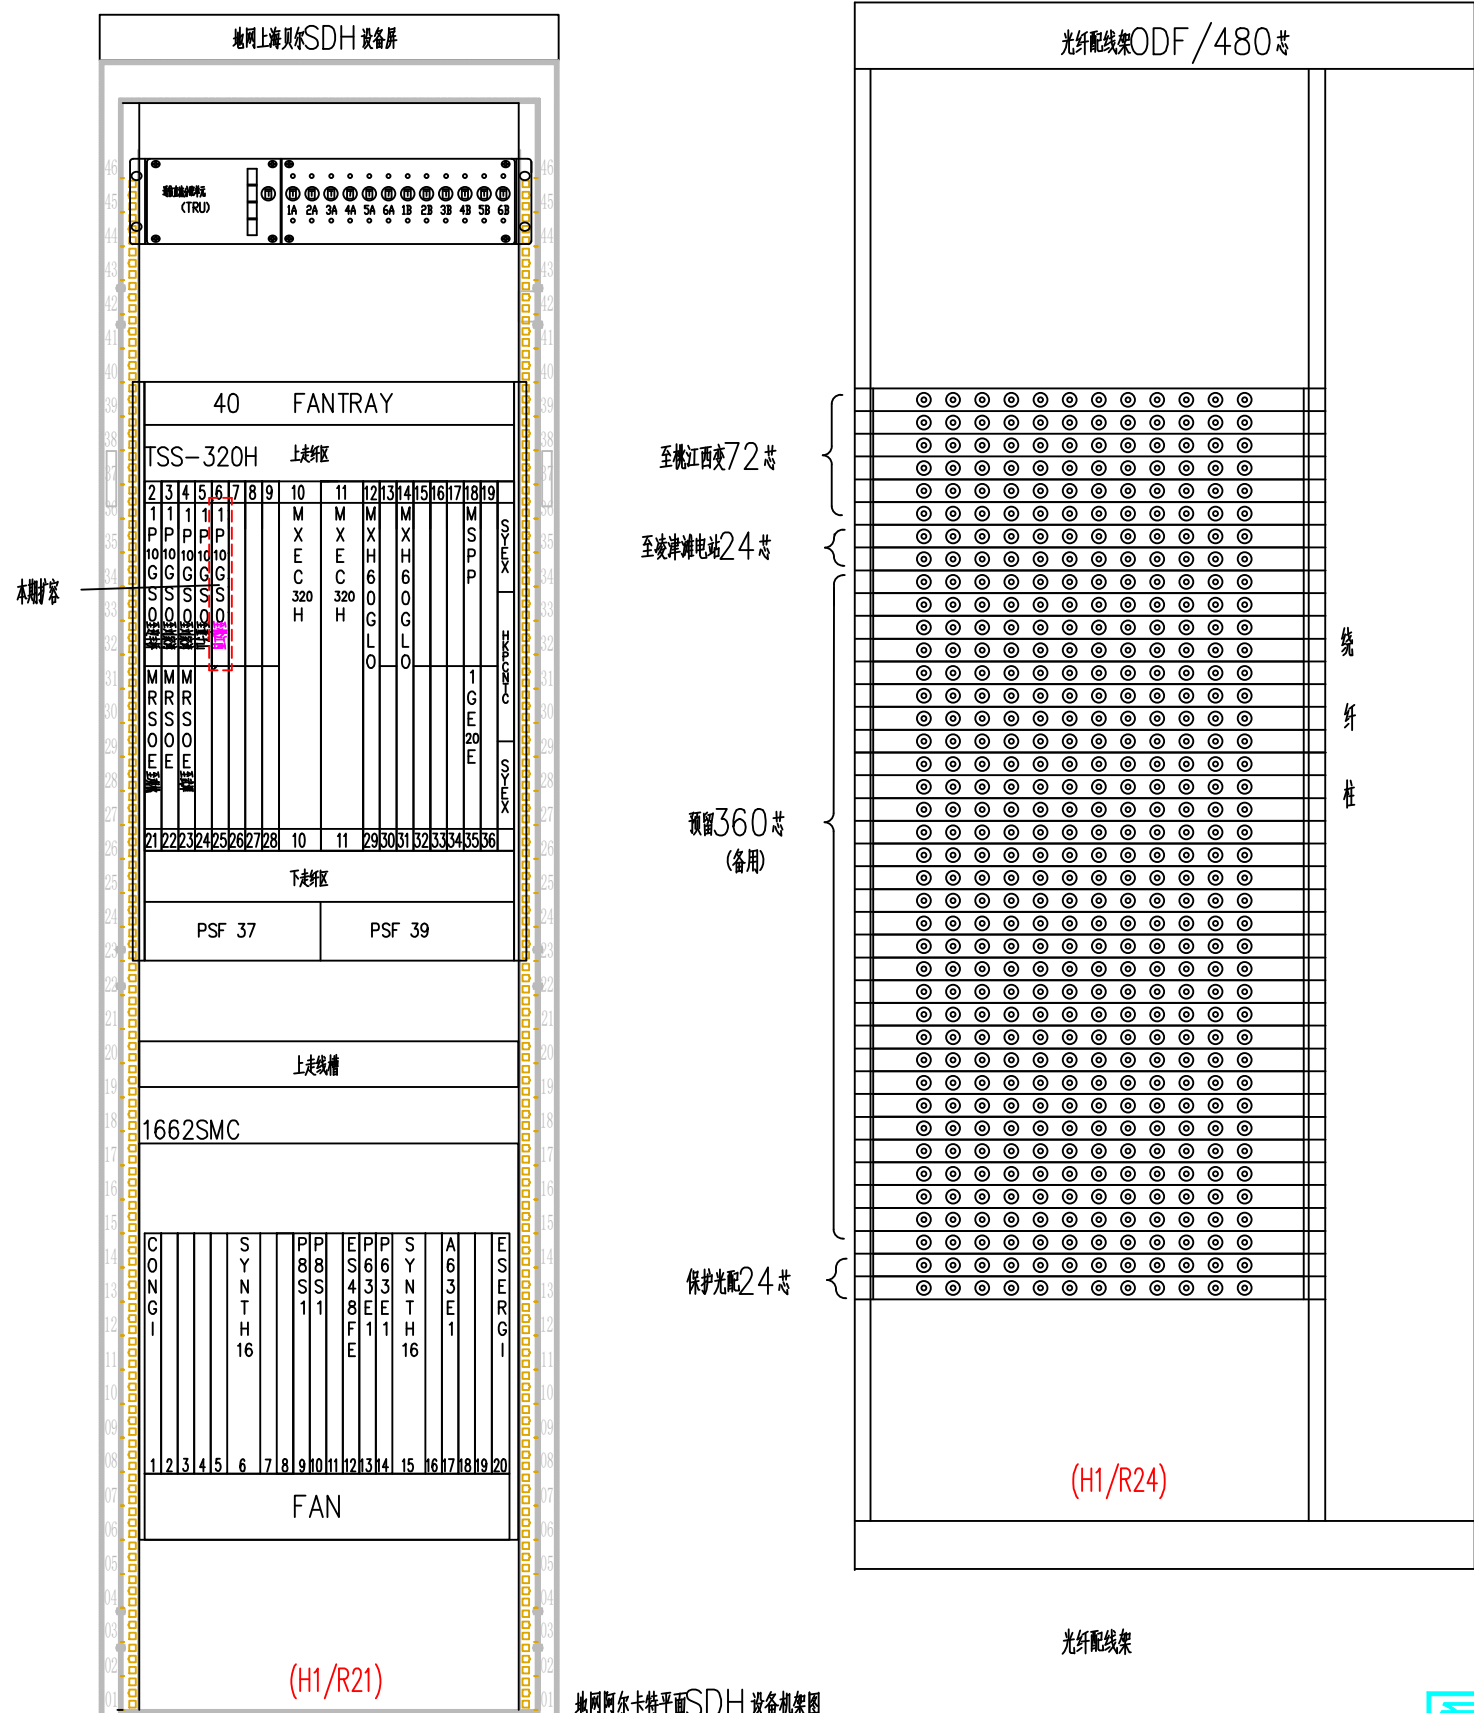

- 注： 1. 桃花江变现有地网阿尔卡特平面SDH设备TSS-320H (R21) 扩容1xSTM-64光接口板1块(含L64.2光模块1块)，对桃江西变，中标厂家：国网信通亿力科技有限责任公司。
2. 本工程在桃花江变新上一个光纤配线架 (ODF/480D)，屏柜尺寸2260x800x600mm，建议放在R24。中标厂家：北京国电通网络技术有限公司。
3. 本图依据设备厂家提供资料编制，请根据现场到货情况调整至本图布置方式。

主要业务板件型号一览表:

子架	型 号	描 述
TSS320H	PSF	电源板
	FANTRAY	风扇单元
	SYEX	辅助控制板
	HKPCNTC	辅助接口板
	MXEC320H	TSS-320 大容量矩阵板 (1.28T)
	MXH60GLO	通用低阶矩阵单元 (60G)
	1P10GS0 (E)	1x10G光接口板 (XFP)
	MRSOE	8x155/622M或4x2.5G 光接口板 (XFP)
	MSPP	以太网业务处理板
1662SMC	1GE20E	20xGE 以太网接口板
	10SD10G	10x10G光接口板 (XFP)
	CONGI	电源及公共接口板1
	ESERGI	电源及公共接口板2
	FAN	散热风扇
	SYNTH16	系统主控交叉板 (2.5G)
	A63E1	63路E1/T1 电接口板
	P63E1	63路E1/T1 支路业务处理板 (保护板)
	P8S1-4E	8xSTM-1/2xSTM-4 光接口板
	ES4-8FE	8路E 以太网交换板 (622M)
	ES16-8FE	8路E 以太网交换板 (2.5G)
	C0-16	双槽位光接口板 (2.5G)

 湖南经研电力设计有限公司				/工程		施工图设计阶段
批准		设计/勘测		地网SDH设备及ODF架机架布置图(桃花江变)		
审核		比例				
校核		日期		图号	BA22015S-U0101-33	

服务承诺：接到您通知1小时内予以答复并及时提供工代服务。投诉电话：0731-85948331，0731-85948342。