


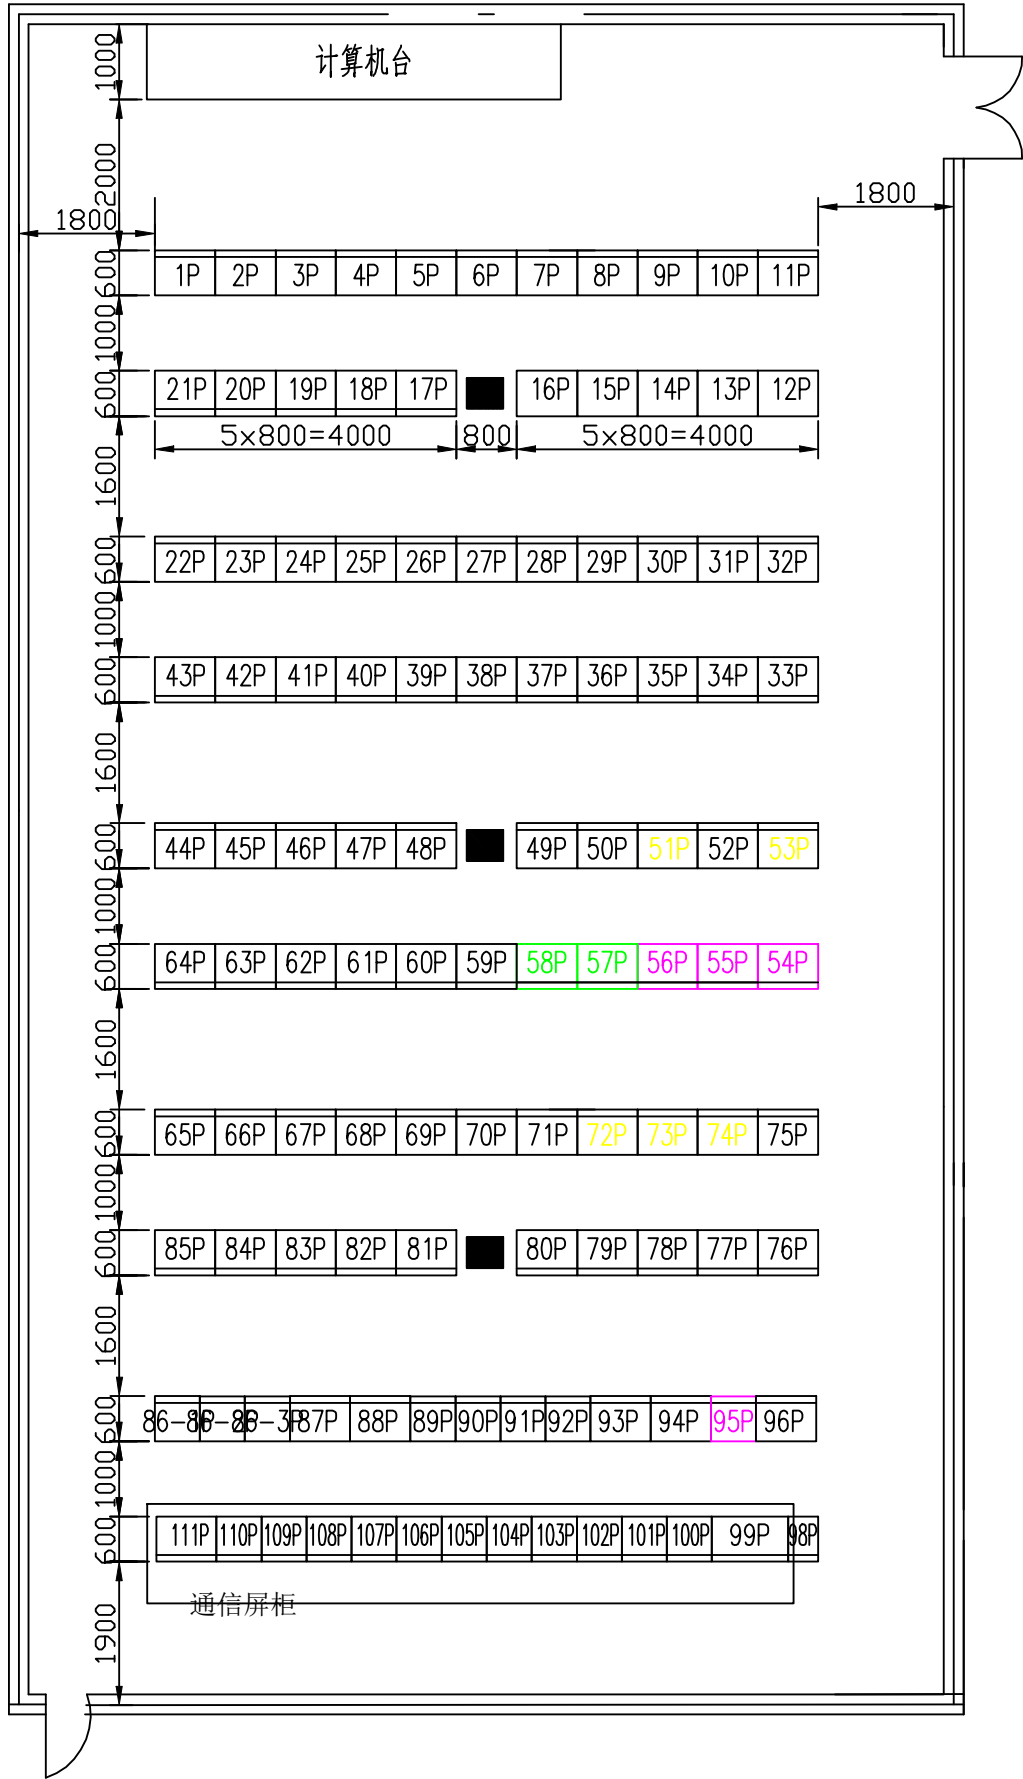

屏号	名 称	本期工程量
88P	省网A2平面中兴SDH S385 设备屏	本期扩容光接口板
89P	通信设备柜 (无线4G 网)	
90P	地网1660 设备屏	本期扩容光接口板
91P	地网OTN 设备屏 (二)	
92P	地网OTN 设备屏 (一)	
98P	华为SDH 设备屏	本期扩容光接口板
99P	光纤配线屏	本期扩容光配模块
100P	省网光纤通信屏	
101P	地网光纤通信屏	
102P	数字配线屏	
103P	地网PCM 设备屏	
104P	省网PCM 设备屏	
105P	音频保安配线屏	
106P	通讯直流电源屏 (一)	
107P	通讯直流馈线屏 (一)	
108P	通讯直流馈线屏 (二)	
109P	通讯直流电源屏 (二)	
111P	综合数据屏	

湖南经研电力设计有限公司				/工程		施工图设计阶段
批准		设计/勘测		二次设备室屏位布置图 (刘家湾变)		
审核		比例				
校核		日期		图号	BA22015S-U0101-36	