
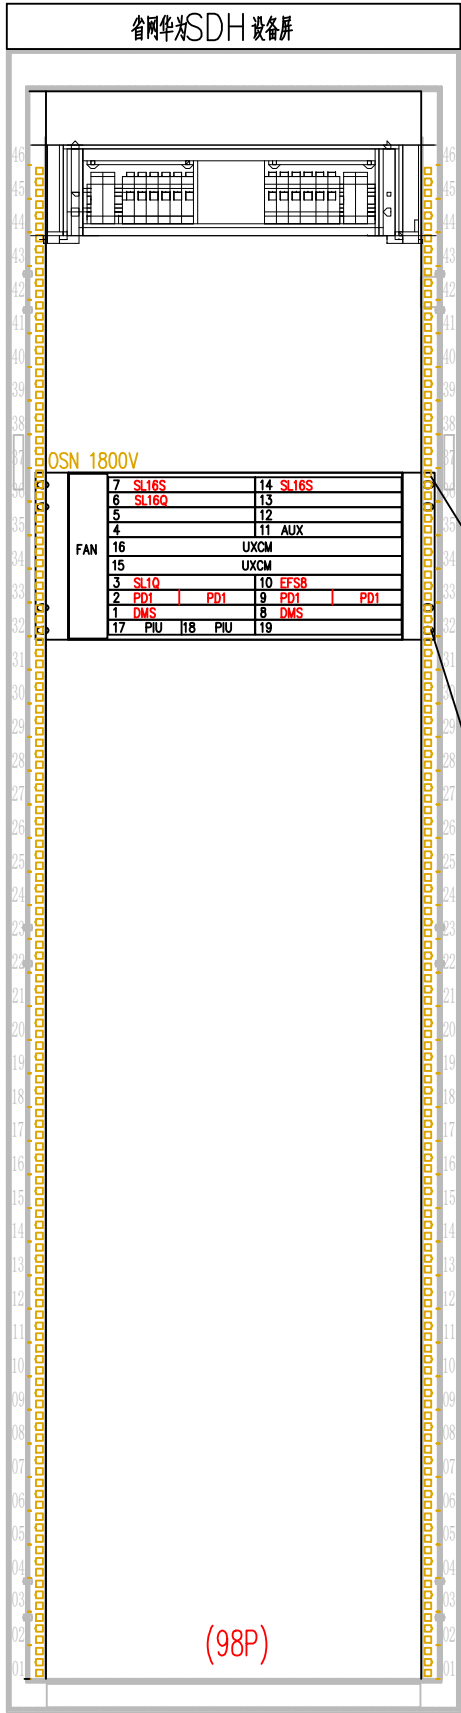


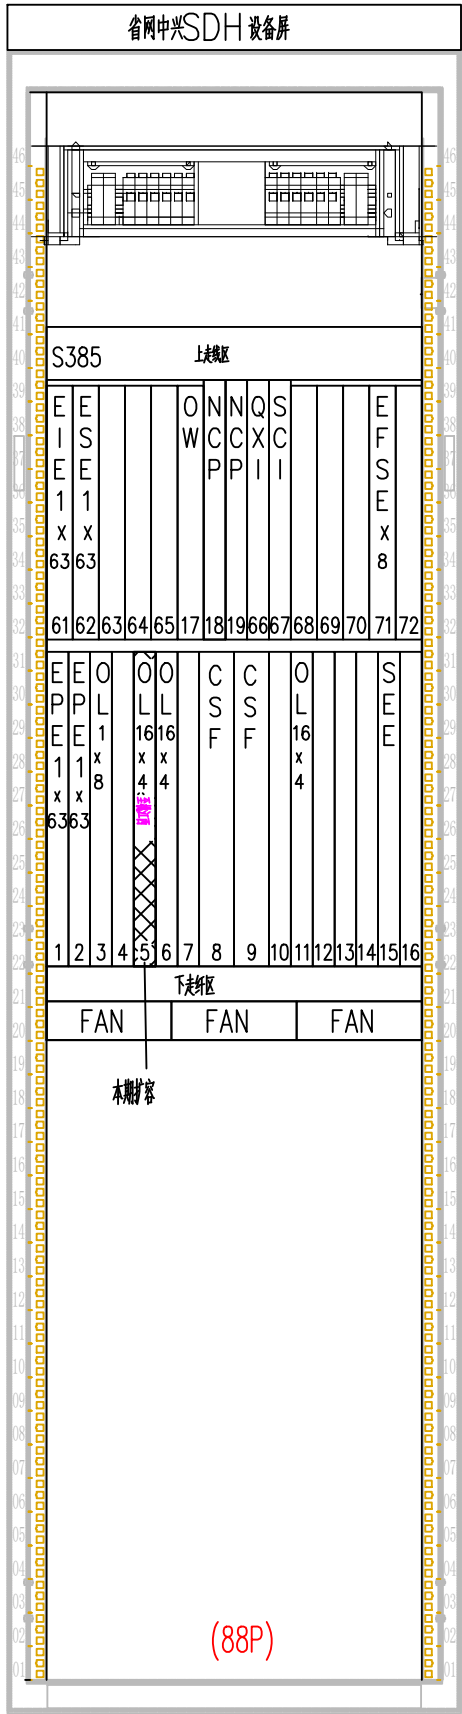

主要业务板件型号一览表:

| 子架        | 型 号   | 描 述                      |
|-----------|-------|--------------------------|
| OSN 1800V | PIU   | 电源板                      |
|           | UXCM  | 主控交叉时钟合一板                |
|           | FAN   | 散热风扇                     |
|           | AUX   | 辅助接口板                    |
|           | DMS   | 32路E1/T1 电接口板            |
|           | PD1   | 32路E1/T1 支路业务处理板 (保护板)   |
|           | EFS8  | 8路E 以太网交换处理板             |
|           | SL1Q  | 4路STM-1 线路处理板            |
|           | SLNO  | STM-16/STM-4/STM-1 业务处理板 |
|           | SL410 | 8路STM-4/STM-1 业务处理板      |
|           | SL16Q | 4路STM-16 线路处理板           |
|           | SL64S | 1路STM-64 线路处理板           |

| 子 述 架 | 型 号     | 描 述                |
|-------|---------|--------------------|
| S385  | FAN     | 散热风扇               |
|       | OW      | 公务板                |
|       | NCP     | 网元控制板              |
|       | QXI     | 管理接口板              |
|       | SCI     | 时钟接口板              |
|       | CSF     | F 型交叉与时钟处理板 (240G) |
|       | ESE1x63 | 63路2M 接口板          |
|       | EIE1x63 | 63路2M 接口铜换板        |
|       | EPE1x63 | 63路2M 处理板          |
|       | ESFE x8 | 8路以太网电接口板          |
|       | SEC     | 以太网处理板             |
|       | OL64    | 1xSTM-64 光线路板      |
|       | OL16    | 1xSTM-16 光线路板      |
|       | OL4x4   | 4xSTM-4 光线路板       |
|       | OL1x4   | 4xSTM-1 光线路板       |

- 注: 1. 刘家湾变现有省网A1平面SDH 设备OSN 1800V (98P) 扩容4xSTM-16 光接口板1 块(含16.2 光模块1 块), 对桃江西变。
2. 刘家湾变现有省网A2平面SDH 设备S385 (88P) 扩容4xSTM-16 光接口板1 块(含16.2 光模块1 块), 对桃江西变。
3. 本图依据设备厂家提供资料编制, 请根据现场到货情况调整至本图布置方式。

|   |  |       |  |                    |                   |         |
|---|--|-------|--|--------------------|-------------------|---------|
|  湖南经研电力设计有限公司 |  |       |  | /工程                |                   | 施工图设计阶段 |
| 批准                                                                                                 |  | 设计/勘测 |  | 省网SDH设备机架布置图(刘家湾变) |                   |         |
| 审核                                                                                                 |  | 比例    |  |                    |                   |         |
| 校核                                                                                                 |  | 日期    |  | 图号                 | BA22015S-U0101-37 |         |