


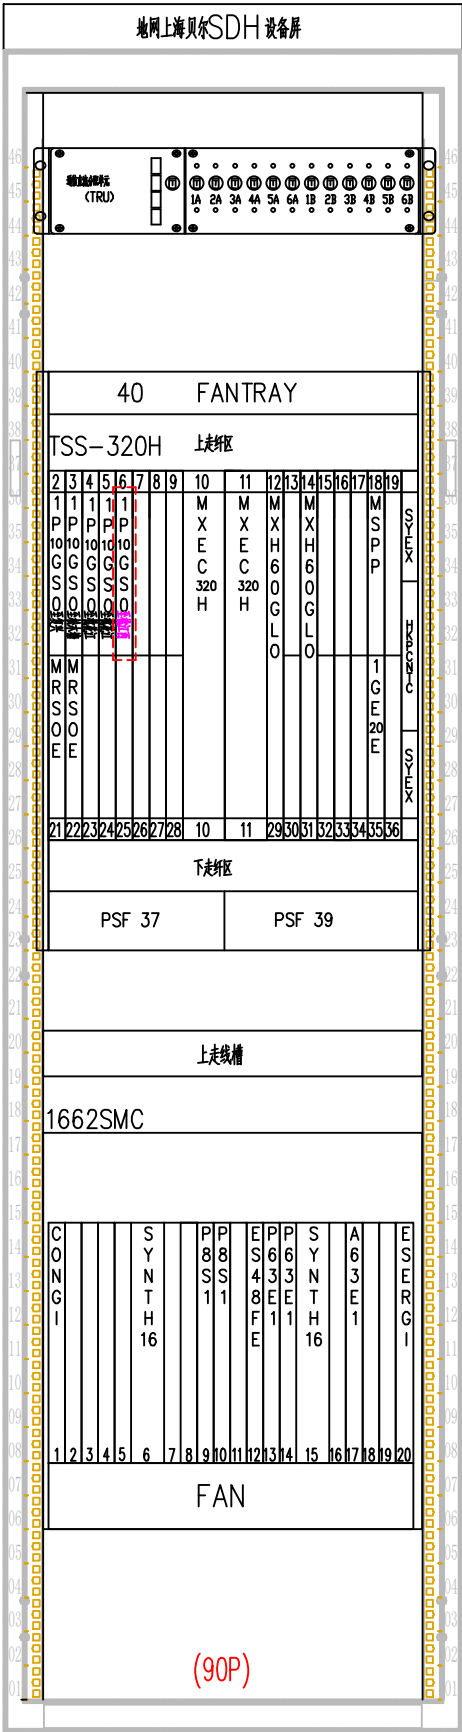

主要业务板件型号一览表:

子架	型 号	描
TSS320H	PSF	电源板
	FANTRAY	风扇单元
	SYEX	辅助控制板
	HKPCNTC	辅助接口板
	MXEC320H	TSS—320 大容量矩阵板 (1.28T)
	MXH60GLO	通用低阶矩阵单元 (60G)
	1P10GS0 (E)	1x10G 光接口板 (XFP)
	MRSOE	8x155/622M 或 4x2.5G 光接口板 (XFP)
	MSPP	以太网业务处理板
	1GE20E	20 xGE 以太网接口板
1662SMC	10SD10G	10x10G 光接口板 (XFP)
	CONGI	电源及公共接口板1
	ESERGI	电源及公共接口板2
	FAN	散热风扇
	SYNTH16	系统主控交叉板 (2.5G)
	A63E1	63 路 E1/T1 电接口板
	P63E1	63 路 E1/T1 支路业务处理板 (保护板)
	P8S1—4E	8 x STM—1/2 x STM—4 光接口板
	ES4—8FE	8 路 E 以太网交换板 (622M)
	ES16—8FE	8 路 E 以太网交换板 (2.5G)
	CO—16	双槽位光接口板 (2.5G)

注: 1. 刘家湾变现有地网阿尔卡特平面SDH 设备TSS—320H (90P) 扩容1 x STM—64 光接口板1 块(含164.2 光模块1 块), 对桃江西变, 中标厂家: 国网通信亿力科技有限责任公司。
2. 本图依据设备厂家提供资料编制, 请根据现场到货情况调整至本图布置方式。

湖南经研电力设计有限公司				/工程		施工图设计阶段
批准		设计/勘测		地网SDH设备机架布置图(刘家湾变)		
审核		比例				
校核		日期		图号	BA22015S-U0101-38	