


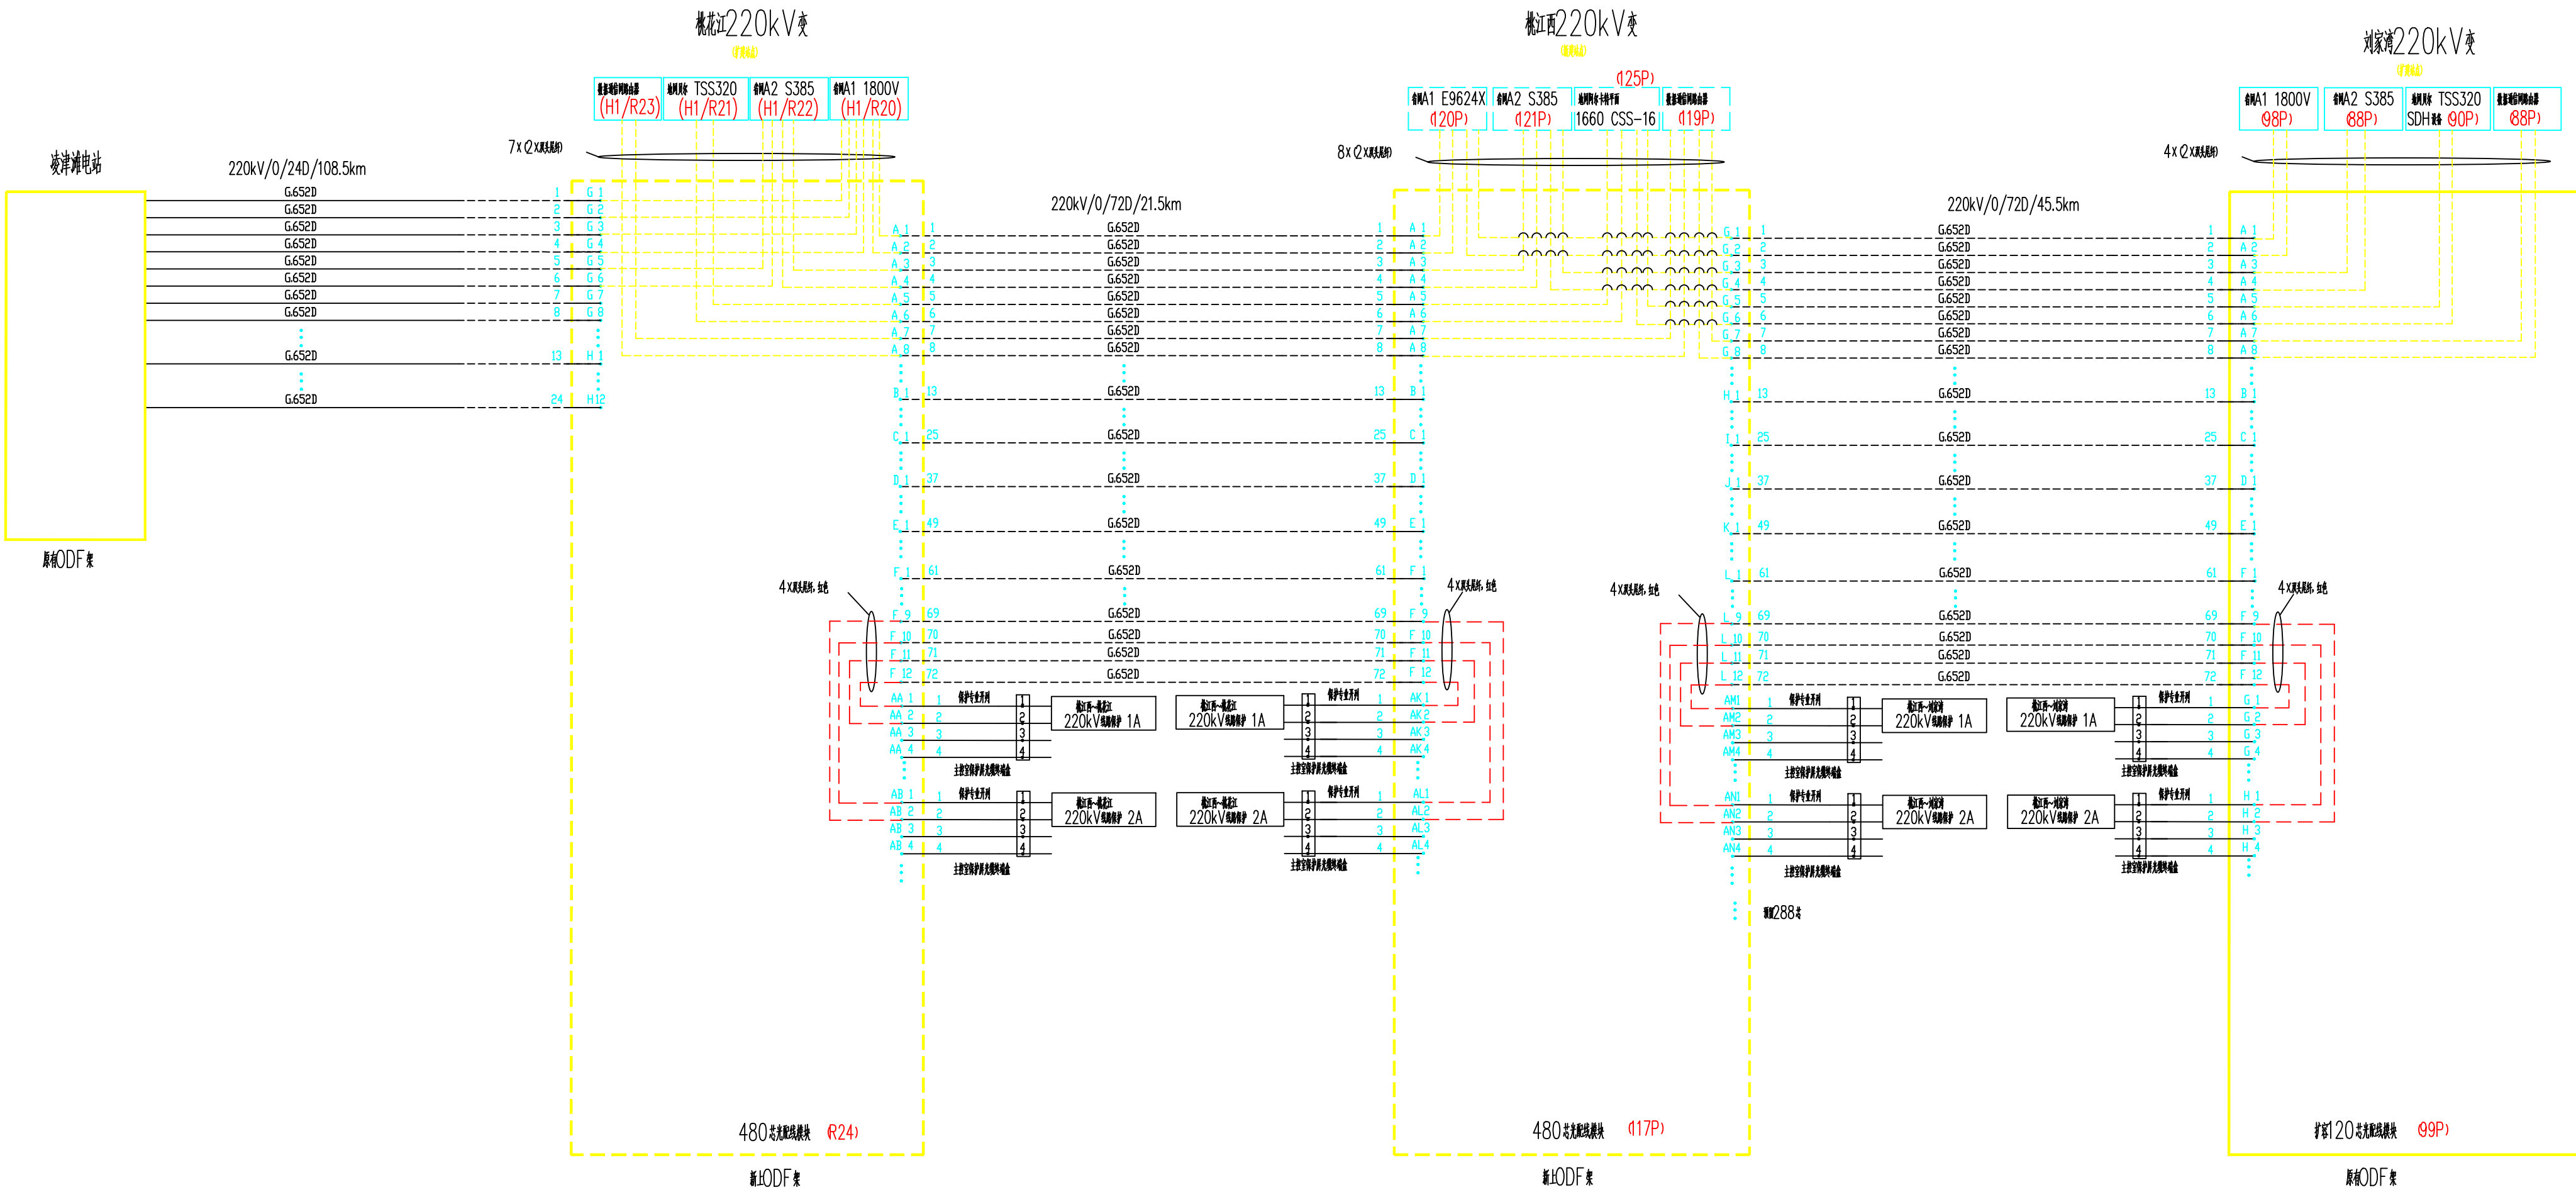

- 备注:
1. 本图只画出与本工程相关光缆线路名称和SDH设备尾纤的连接方式。
 2. 设备的具体纤芯安排以运行单位的工作任务单为准。
 3. 现有光纤和光缆以标出新架ODF模块的顺序编号，其余具体接线模块和端子位置现场实际情况确定。
 4. 保护光缆终端盒安装在相关线路保护屏下，光纤保护装置的光纤由保护装置提供，本设计只画出该部分接线。
 5. 图中虚线为本工程新建设备或光缆，实线表示现有其它工程设备和光缆。

湖南经研电力设计有限公司				/工程		施工图设计阶段
批准		设计/勘测		ODF架配纤示意图		
审核		比例				
校核		日期		图号	BA22015S-U0101-18	