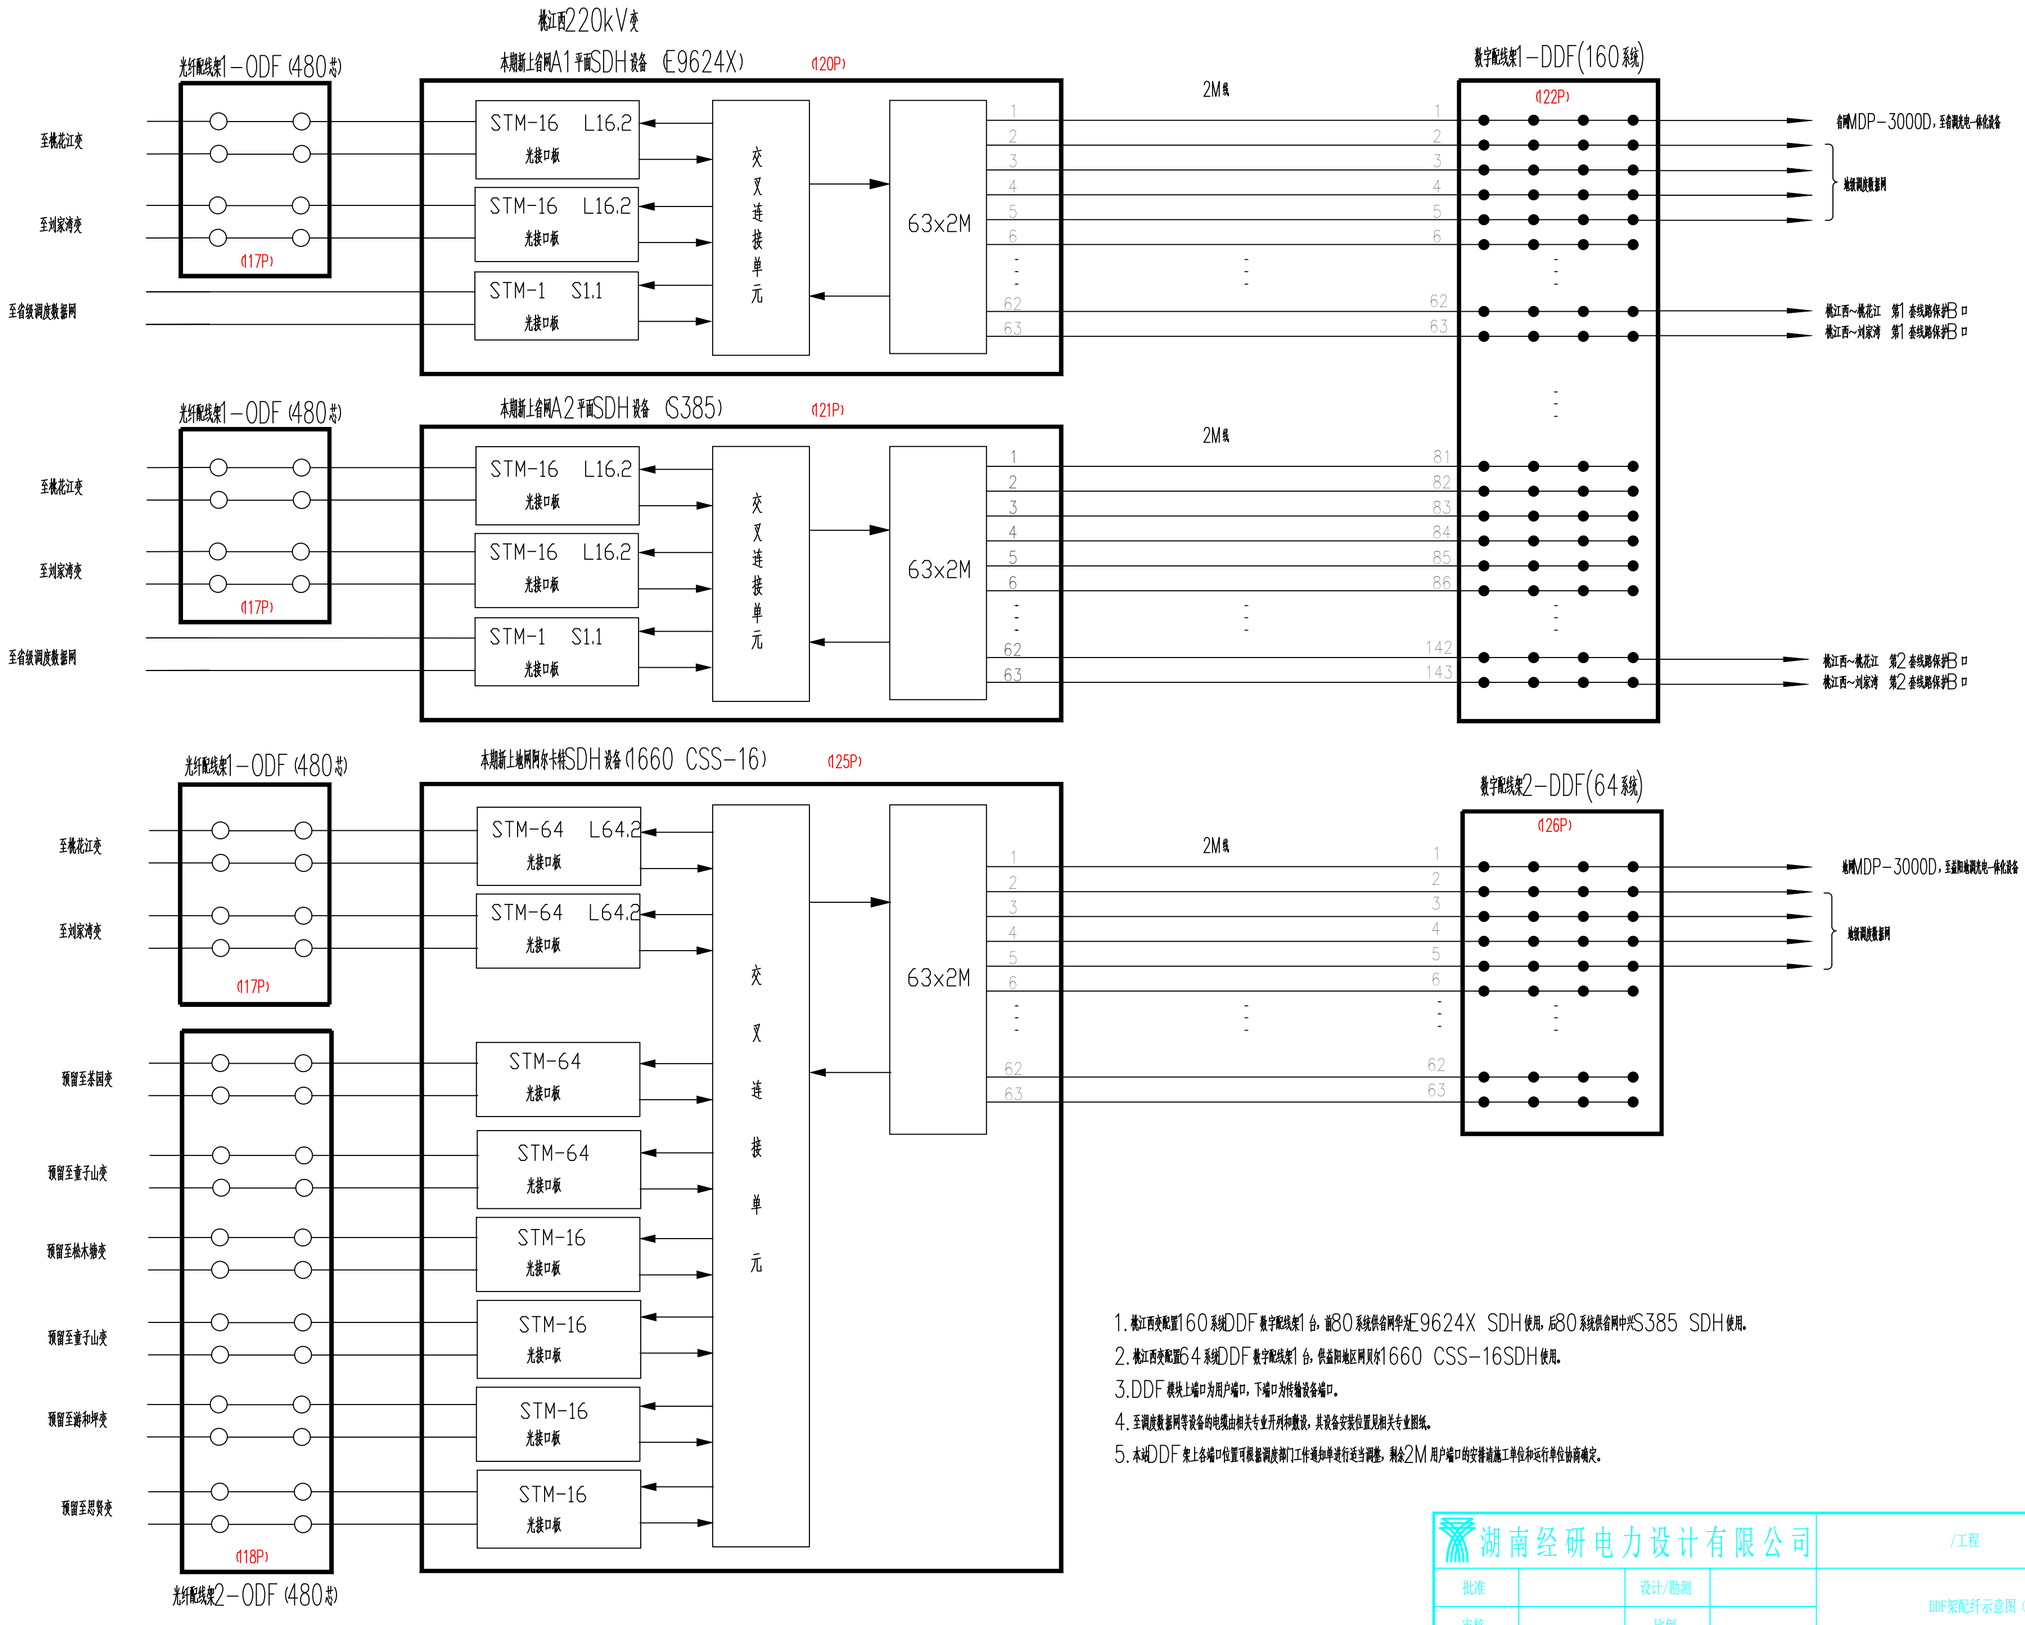

1. 桃江西变配置160系统DDF数字配线架1台，与80系统供省网华为E9624X SDH使用，与80系统供省网中兴S385 SDH使用。
2. 桃江西变配置64系统DDF数字配线架1台，供益阳地区网贝尔1660 CSS-16SDH使用。
3. DDF模块上端口为用户端口，下端口为传输设备端口。
4. 至调度数据网等设备的电缆由相关专业开列和敷设，其设备安装位置见相关专业图纸。
5. 本端DDF架上各端口位置可根据调度部门工作通知单进行适当调整，剩余2M用户端口的安排请施工单位和运行单位协商确定。

湖南经研电力设计有限公司				/工程	施工图设计阶段
批准		设计/勘测		DDF架配纤示意图（桃江西变）	
审核		比例			
校核		日期	/	图号	BA22015S-U0101-19

服务承诺：接到您通知1小时内予以答复并及时提供工代服务。投诉电话：0731-85948331，0731-85948342。