



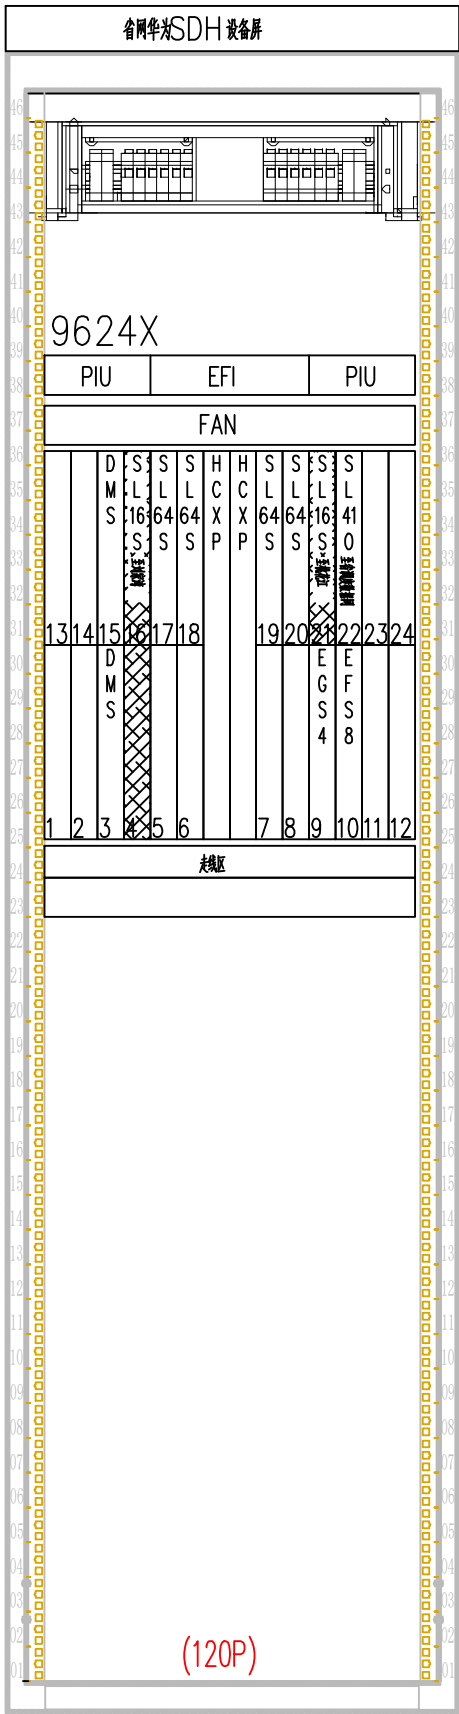

省网A1平面SDH设备机架图

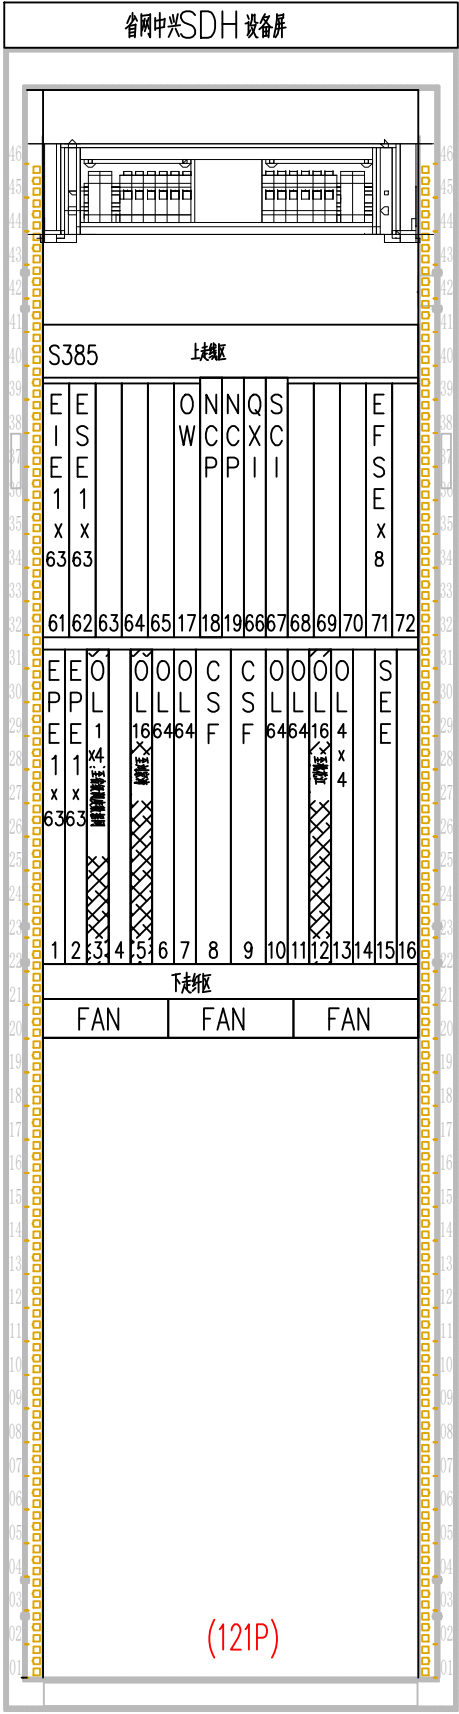

省网A2平面SDH设备机架图

主要业务板件型号一览表:

子架	型 号	描 述
9624X	HCXP	通用交叉、主控、时钟处理板 (220G 高阶/20G 低阶)
	EFI	系统控制与通信板
	PIU	电源接口板
	FAN	风扇板
	SL64S	1xSTM—64 光接口板
	SL16S	1xSTM—16 光接口板
	SL16Q	4xSTM—16 光接口板
	SL4	1xSTM—4 光接口板
	SL410	8*STM—4/STM—1 光接口板
	DMS	2*PD1+1*DMS, 32 路 1:1 保护;
	EGS4	四路交叉式千兆以太网处理板
	EFS8	8 路带交叉功能的快速以太网处理板
	DAP—BA	OACE101, 可插接扩展 C 波段光放/20~31dB/21.5dBm
	DAP—PA	PA30, 可插接扩展 C 波段光放/25dB
	DCM	DCM (E) (偿 G.652 光纤, 补偿 100km)

主要业务板件型号一览表:

子架	型 号	描 述
S385	FAN	散热风扇
	OW	公务板
	NCP	网元控制板
	QXI	管理接口板
	SCI	时钟接口板
	CSF	F 型交叉与时钟处理板 (240G)
	ESE1x63	63 路 2M 接口板
	EIE1x63	63 路 2M 接口倒换板
	EPE1x63	63 路 2M 处理板
	ESFE x8	8 路以太网电接口板
	SEC	以太网处理板
	OL64	1xSTM—64 光线路板
	OL16	1xSTM—16 光线路板
	OL4x4	4xSTM—4 光线路板
	OL1x4	4xSTM—1 光线路板

- 注: 1. 桃江西 220kV 变为省网 A1 平面新上站点, 本期新上省网华为 9624X SDH 设备 1 套, 中标厂家: 安徽继远软件有限公司。
2. 桃江西 220kV 变为省网 A2 平面新上站点, 本期新上省网中兴 S385 SDH 设备 1 套, 中标厂家: 北京国电网络技术有限公司。
3. 新上设备机架尺寸: 2260mm (高) x 600mm (宽) x 600mm (深)。
4. 本图依据设备厂家提供资料编制, 根据现场实际到货情况调整。

湖南经研电力设计有限公司				/工程	施工图设计阶段
批准		设计/勘测		省网 SDH 设备机架布置图 (桃江西变)	
审核		比例			
校核		日期		图号	BA22015S-U0101-20