


主要业务板件型号一览表:

子 架	型 号	描 述
阿尔卡特 1660 CSS-16	S60ADC	直流电源单板
	SAUX12	辅助接口板
	S6FAN	风扇
	CORE-16h	交叉时钟板 (240G)
	MC20	控制板
	A42E1	42 路E1 电接口板
	P42E1	42 路E1 业务处理板
	P1S64	1xSTM-64 光接口板
	P4S16	4xSTM-16 光接口板
	E8FE	8 路FE 以太网交换板
	P4GE	4 路GE 以太网交换板
	P8S1	8xSTM-1 光接口板

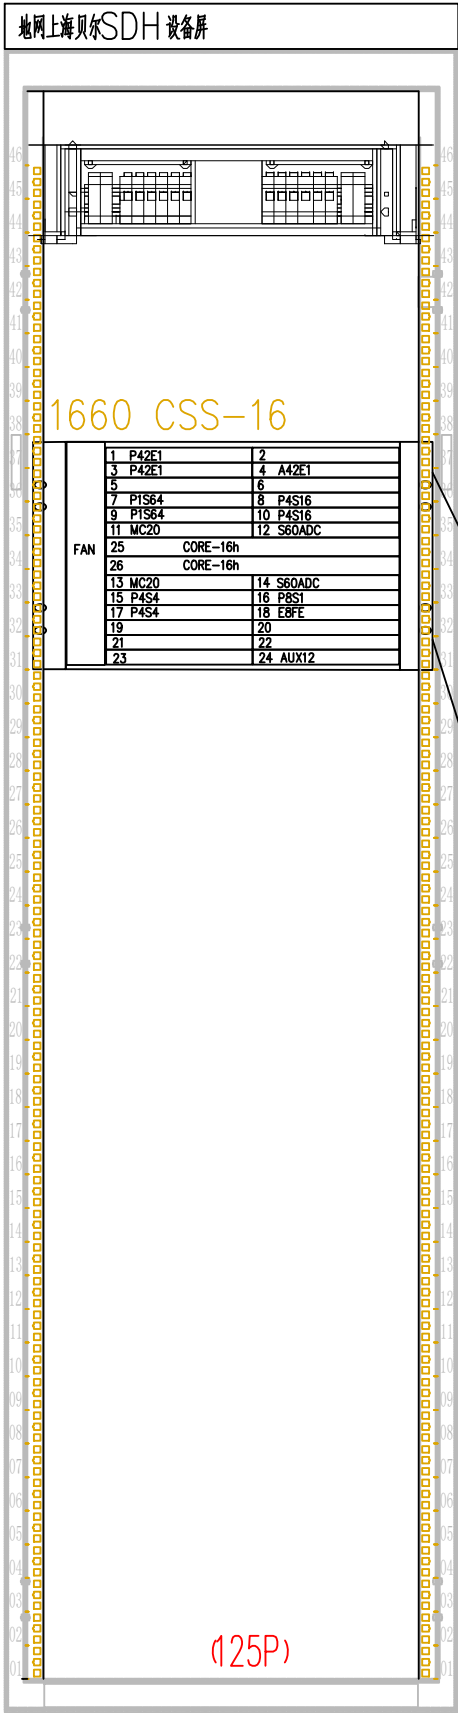

局部放大:

FAN	1	P42E1	2	
	3	P42E1	4	A42E1
	5		6	
	7	P2S64 至桃花江、预留至茶园	8	P1S16 预留至童子山
	9	P2S64 至刘家湾、预留至童子山	10	P1S16 预留至松木塘
	11	MC20	12	S60ADC
	25	CORE-16h		
	26	CORE-16h		
	13	MC20	14	S60ADC
	15	P4S16 预留至游和坪、思贤	16	
	17	P4S4	18	E8FE
	19		20	
	21		22	
	23		24	AUX12

- 注: 1. 桃江西220kV变为地网阿尔卡特平面新上站点, 本期新上益阳地网阿尔卡特1660 CSS-16 SDH 设备 1套, 中标厂家: 国网信通亿力科技有限责任公司。
2. 新上设备机架尺寸: 2260mm (高)x600mm (宽)x600mm (深)。
3. 本图依据设备厂家提供资料编制, 根据现场实际到货情况调整。

湖南经研电力设计有限公司				/工程		施工图设计阶段
批准		设计/勘测		地网SDH设备机架布置图(桃江西变)		
审核		比例				
校核		日期		图号	BA22015S-U0101-21	