




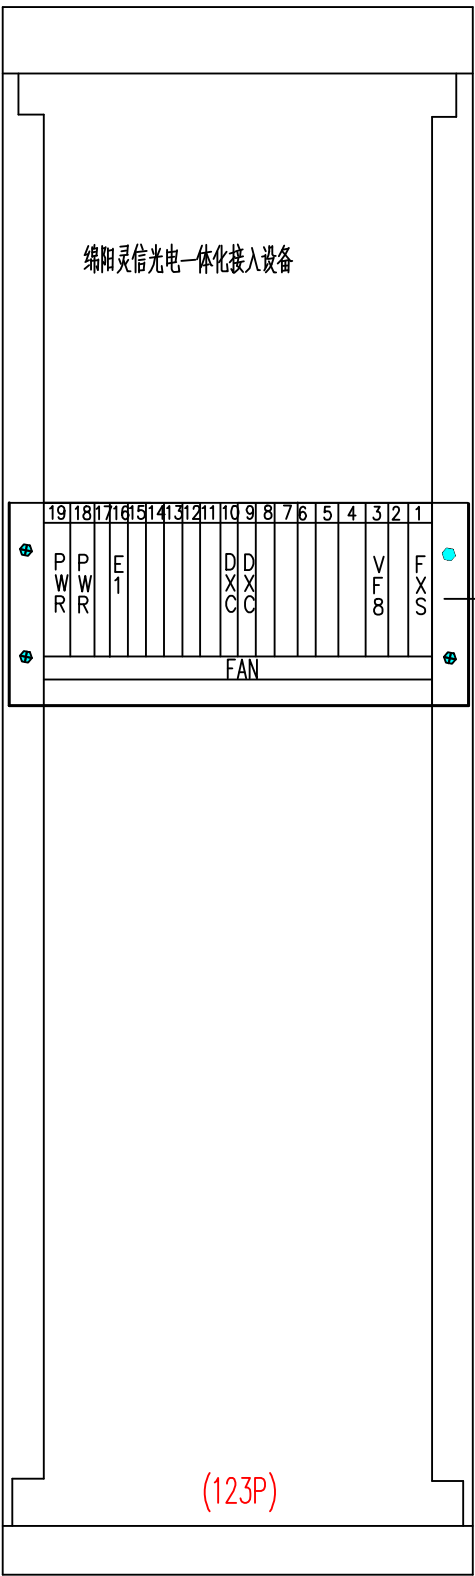

省网光电一体化设备机架图

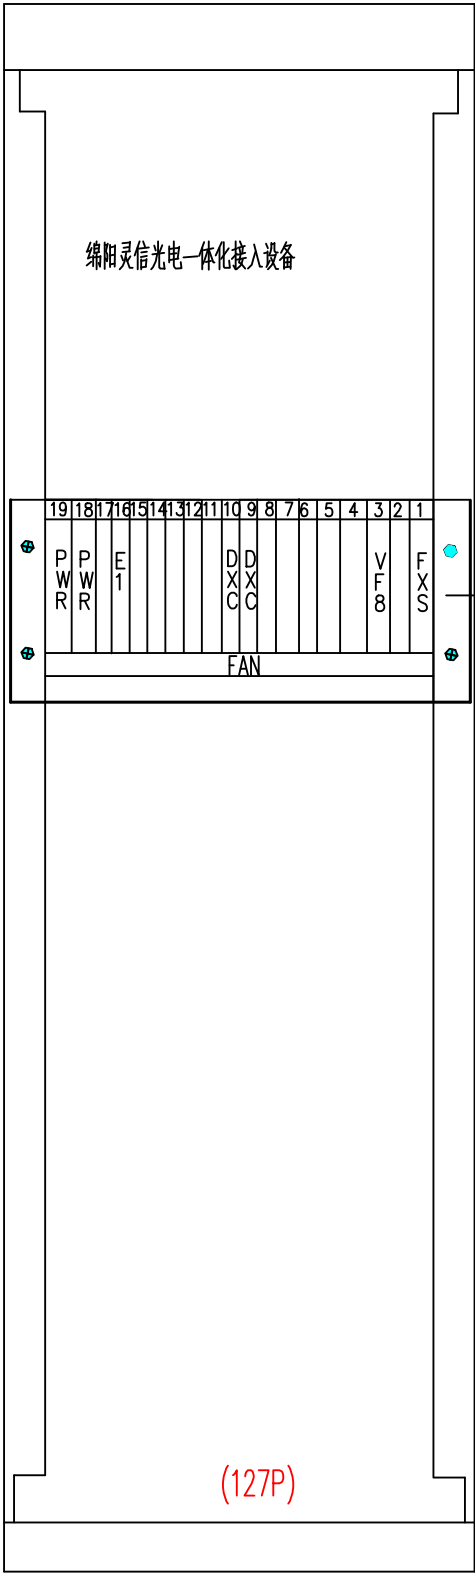

地网光电一体化设备机架图

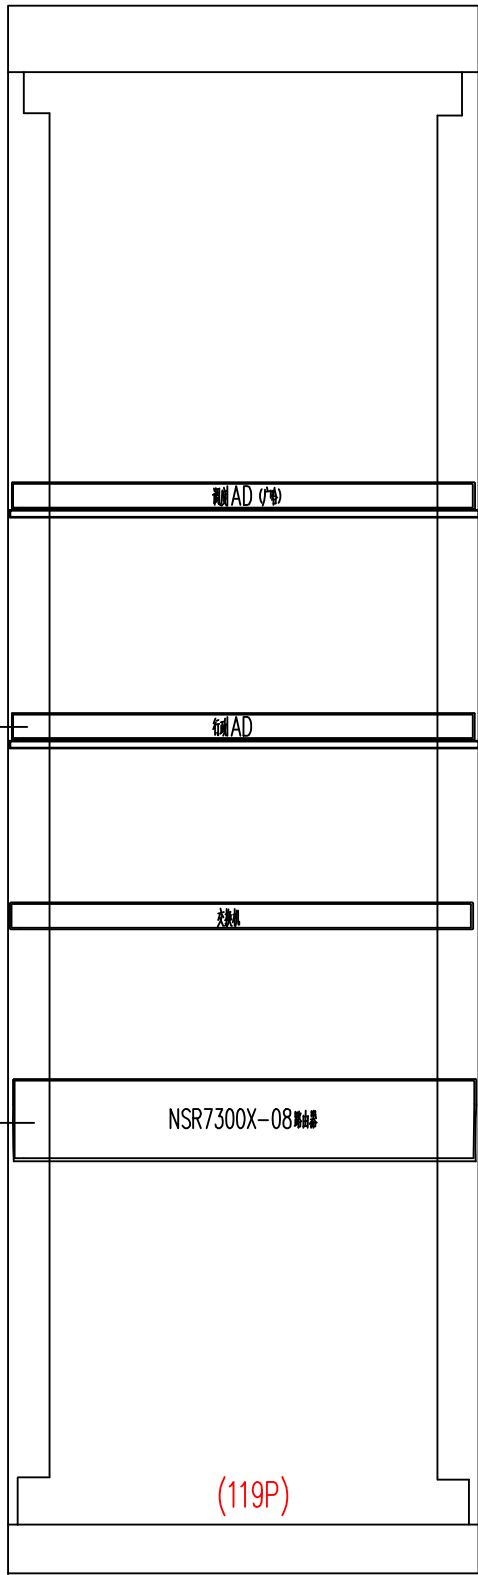

数据通信设备机架图

主要业务板件型号一览表 (123P/125P):

| 序号  | 名称      | 型号                 | 单位 | 数量 |
|-----|---------|--------------------|----|----|
| 1   | 光电一体化设备 | 绵阳灵信MDP-3000D      | 套  | 1  |
| 1.1 | 交叉板     | DXC                | 块  | 2  |
| 1.2 | 电源板     | PWR                | 块  | 2  |
| 1.3 | E1板     | E1,8路/板            | 块  | 1  |
| 1.4 | FXS二线板  | FXS,16路/板          | 块  | 1  |
| 1.5 | VF8四线板  | VF8,8路/板           | 块  | 1  |
| 2   | 机柜及附件   | 2260mm*600mm*600mm | 面  | 1  |

主要业务板件型号一览表 (120P):

| 序号  | 名称      | 型号                  | 单位 | 数量 |
|-----|---------|---------------------|----|----|
| 1   | 数据通信网设备 |                     |    |    |
| 1.1 | 路由器     | NSR7300X-08         | 台  | 1  |
| 1.2 | 交换机     | 低端                  | 台  | 1  |
| 1.3 | 光接口模块   | 光模块, 千兆单模, 80km     | 个  | 2  |
| 1.4 | 光接口模块   | 光模块, 千兆单模, 40km     | 个  | 2  |
| 1.5 | 光接口模块   | 光模块, 千兆多模, 0.5km    | 个  | 4  |
| 2   | IAD设备   |                     | 台  | 2  |
| 3   | 机柜及附件   | 2260mm*600mm*1200mm | 面  | 1  |

注: 1. 桃江西220kV变为新上站点, 本期新上省网光电一体化接入设备MDP-3000D 1套、地网光电一体化接入设备MDP-3000D 1套 (中标厂家: 绵阳灵信电子有限责任公司), 机柜尺寸皆为2260mm (含60mm 楣, 高)x600mmx600mm。本图未画出湖南省调、益阳地调的光电一体化设备, 益阳地调光电一体设备扩容FXO板、MP板各1块。

2. 桃江西220kV变本期新上数据通信网路由器NSR7300X-08 1台 (中标厂家: 许继电气股份有限公司), 数据通信网交换机1台 (中标厂家: 北京中电飞华通信有限公司), 调度 IAD设备1台 (中标厂家: 四川景皓科技有限责任公司), 行政 IAD设备1台 (中标厂家: 湖南星通电力信息通信有限公司), 合柜安装, 机柜尺寸为2260mm (含60mm 楣, 高)x600mmx1200mm。

3. 新上设备具体板件安装槽位请参见厂家安装说明书及运行单位工作通知单。

|   |  |       |  |                          |                   |         |  |
|---|--|-------|--|--------------------------|-------------------|---------|--|
|  湖南经研电力设计有限公司 |  |       |  | /工程                      |                   | 施工图设计阶段 |  |
| 批准                                                                                                 |  | 设计/勘测 |  | 光电一体化设备及数据通信网机架布置图(桃江西变) |                   |         |  |
| 审核                                                                                                 |  | 比例    |  |                          |                   |         |  |
| 校核                                                                                                 |  | 日期    |  | 图号                       | BA22015S-U0101-22 |         |  |