



省网A1平面光纤通信网络现状图

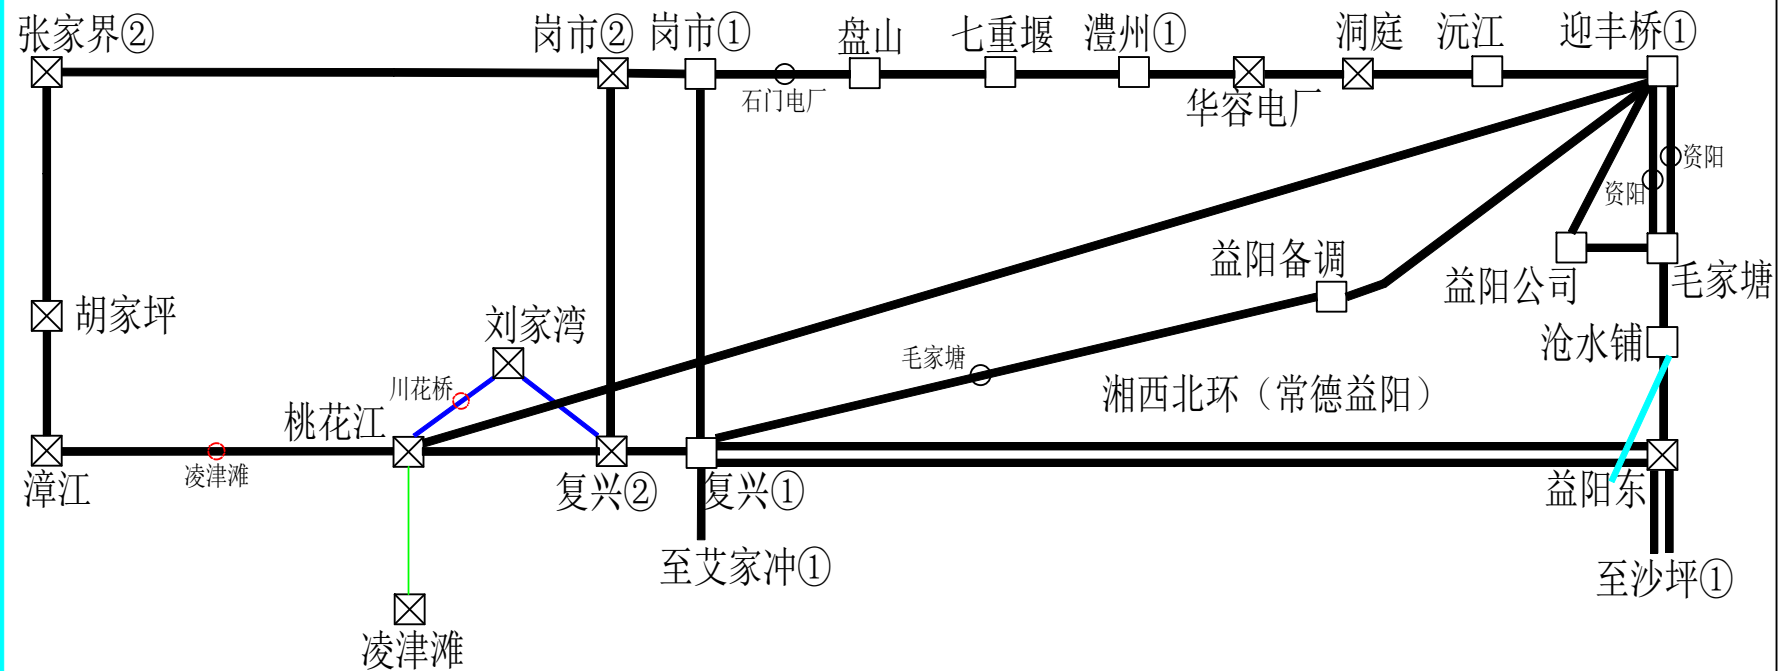


省网A2平面光纤通信网络现状图

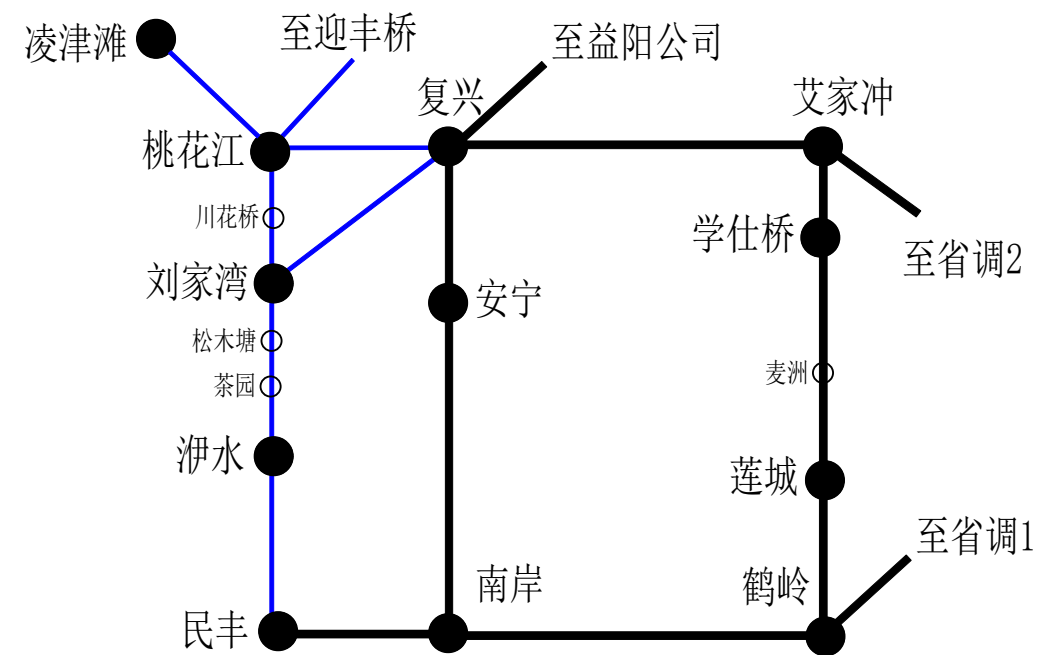


省网A1平面光纤通信网络组织图

(本期建设)

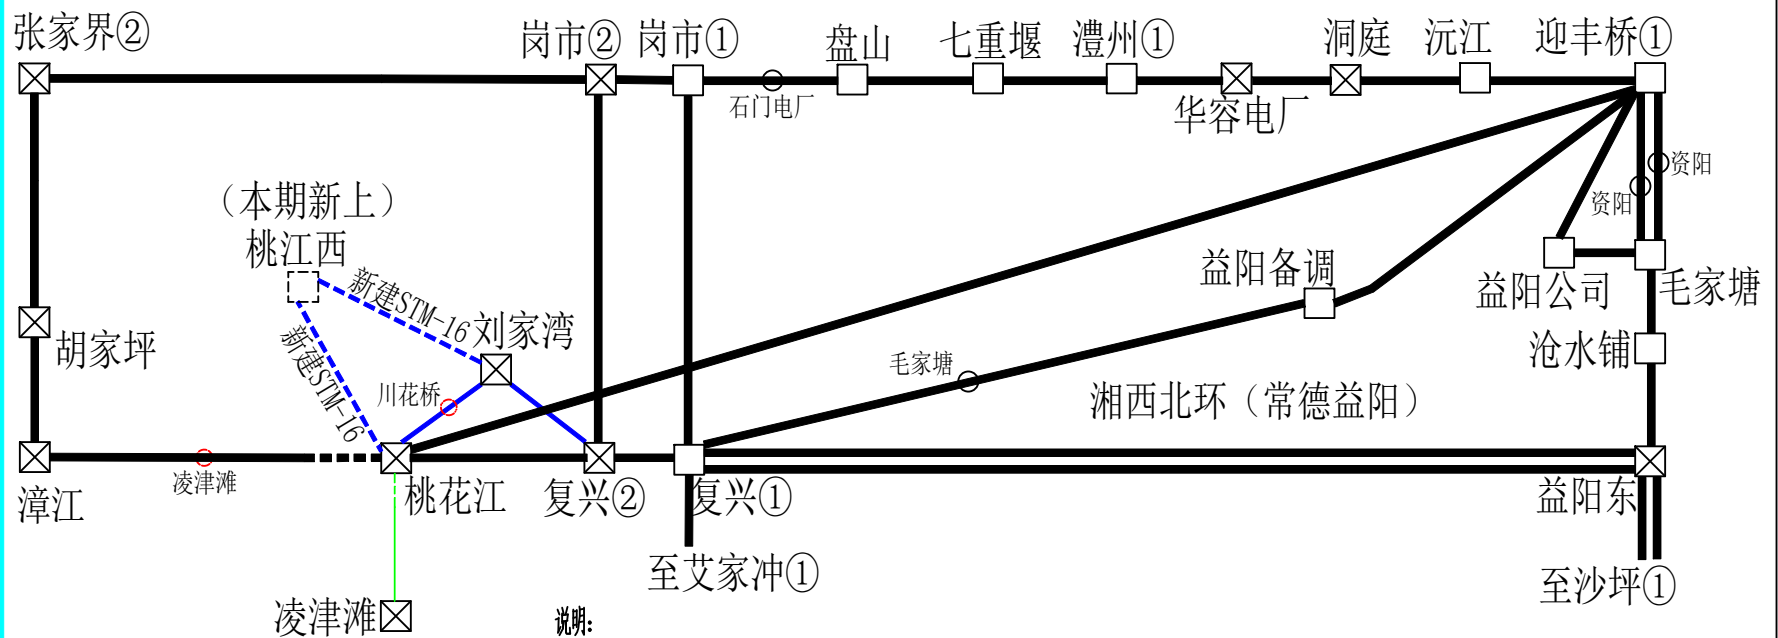

省网A2平面光纤通信网络组织图

(本期建设)

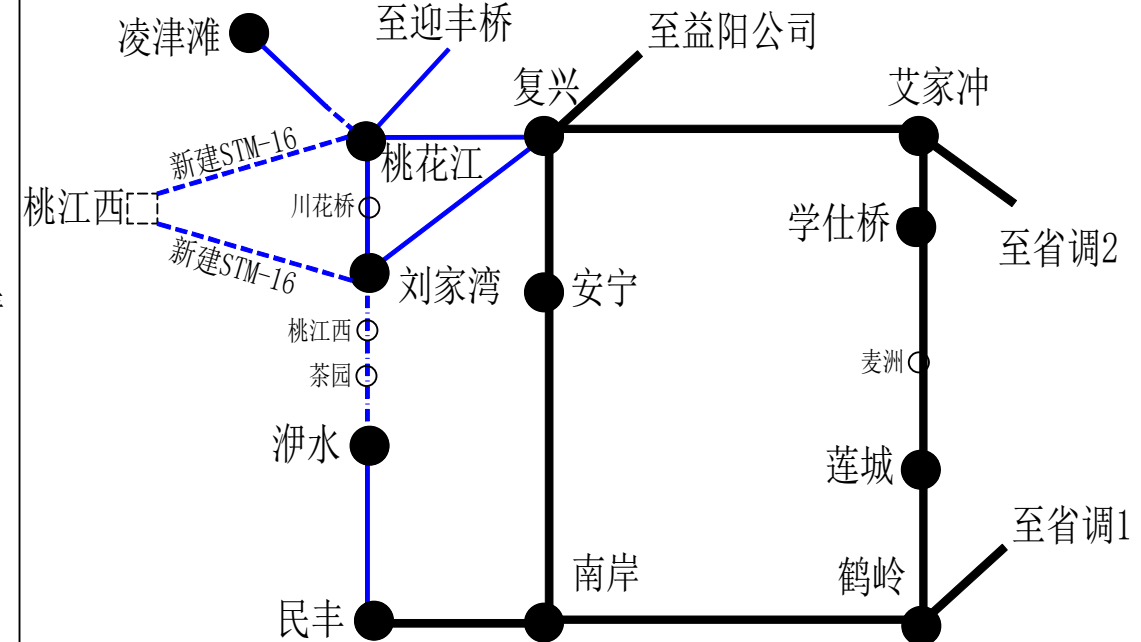

说明:

- 2、本期新建省网A1平面刘家湾~桃江西~桃花江STM-16光纤通信电路(光口按1+0配置),恢复漳江~桃花江STM-64、凌津滩~桃花江STM-1光纤通信电路。3、本期新建省网A2平面刘家湾~桃江西~桃花江STM-16光纤通信电路(光口按1+0配置),恢复凌津滩~桃花江STM-16光纤通信电路。

图 例

-  OSN 7500设备  STM-64电路
 OSN 1800V设备  STM-16电路
 中兴S385设备  STM-1电路
 本工程新上10G设备  跳纤站



/工程

施工图设计阶段

批准

设计/勘测

比例

日期

省网SDH光纤通信网络方案图

BA22015S-U0101-04